

Altura	Peso	ALMA	MESA	SISO X	SISO Y
mm	kg/m	mm	mm	mm	mm
10	0,10	75,20	4,22	28,31	6,53
20	0,20	75,20	8,44	56,62	13,06
30	0,30	75,20	12,66	84,93	19,59
40	0,40	75,20	16,88	113,24	26,12
50	0,50	75,20	21,10	141,55	32,65
60	0,60	75,20	25,32	169,86	39,18
70	0,70	75,20	29,54	198,17	45,71
80	0,80	75,20	33,76	226,48	52,24
90	0,90	75,20	37,98	254,79	58,77
100	1,00	75,20	42,20	283,10	65,30

DETALHE - TABELA DOS PERFIS TIPO "U"

Altura	Peso	ALMA	MESA	SISO X	SISO Y
mm	kg/m	mm	mm	mm	mm
10	0,10	75,20	4,22	28,31	6,53
20	0,20	75,20	8,44	56,62	13,06
30	0,30	75,20	12,66	84,93	19,59
40	0,40	75,20	16,88	113,24	26,12
50	0,50	75,20	21,10	141,55	32,65
60	0,60	75,20	25,32	169,86	39,18
70	0,70	75,20	29,54	198,17	45,71
80	0,80	75,20	33,76	226,48	52,24
90	0,90	75,20	37,98	254,79	58,77
100	1,00	75,20	42,20	283,10	65,30


DETALHE - TABELA DE REFERÊNCIA DE PERFIL "I"

Dimensão nominal	Dimensão nominal	Dimensão nominal	Dimensão nominal	Dimensão nominal	Dimensão nominal
Dimensão nominal	Dimensão nominal	Dimensão nominal	Dimensão nominal	Dimensão nominal	Dimensão nominal
1,75	2	2	2,5	2,5	2,5
19	22	24	27	30	32
7,68	8,98	10,18	11,72	12,72	14,22
16	165	00	0,2		
20	407	00	0,2		
25	459	00	0,2	559	00
30	461	00	0,2	561	00
35	462	00	0,2	562	00
40	463	00	0,2	563	00
45	464	00	0,2	564	00
50	465	00	0,2	565	00

DETALHE - TABELA DE PARAFUSOS REFERÊNCIA

b	Peso Nominal	t	Área	I _{xx} /cm ⁴	W _x /cm ³	I _{yy} /cm ⁴	W _y /cm ³	I _{zz} /cm ⁴	x
pol	mm	kg/m	mm	cm ⁴	cm ³	cm ⁴	cm ³	cm	cm
3/4"	19,050	0,97	2,50						
1"	25,400	1,33	3,18						
1 1/4"	31,750	1,69	3,75						
1 1/2"	38,100	2,05	4,32						
2"	50,800	2,71	5,64						

DETALHE - TABELA DE REFERÊNCIA DE CANTONEIRA

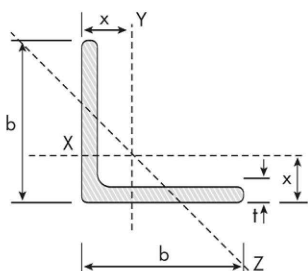

NA PARTE SUPERIOR DEVERÁ SER FEITO A FIXAÇÃO NA ESTRUTURA EXISTENTE EM FORMATO REDONDO TAMBÉM EM ALUMÍNIO


CAIXA EM ALUMÍNIO ACABAMENTO LISO
ESP. 2,5MM DIMENSÕES 54X20X50CM (CONFERIR MEDIDAS IN LOCO)
PREENCHIDA COM ESPUMA EXPANSIVA EPOXI BICOMPONENTE (A+B) COMPONENTES A CAIXA DEVERÁ TER ACESSOS PARA GARANTIR O ACOPLAMENTO E DESACOPLEMENTO DA BOMBA E DEMAIS MANUTENÇÕES, ISSO TEM QUE SER VALIDADO COM A MANUTENÇÃO A CAIXA DEVE SER MOLDADA NO LOCAL

NA PARTE INFERIOR DEVERÁ SER MOLDADA DE ACORDO COM A BASE E FIXADA NA BASE DA BOMBA DÁGUA


DETALHE - CAIXA DE ISOLAMENTO DE CONDENSAÇÃO DO ROTOR DAS BOMBAS DE 20 E 25CV (X6)

Nota das montagens e do aço:


Os perfis de aço estrutural deverão ser em aço ASTM A709/A588), entregues prontos para montagem, já cortados, dobrados e furados conforme o modelo de referência local e o projeto. A proteção anticorrosiva deve ser aplicada em fábrica, compreendendo limpeza de superfície e um sistema de pintura industrial de três camadas, sendo obrigatória a utilização de primer epóxi, camada intermediária epóxi de alta espessura e acabamento final em poliuretano (PU), sendo obrigatório a entrega das peças íntegras, a inspeção e o reatque de danos à pintura no pós-instalação. Adicionalmente, deve ser realizado o escoramento da estrutura existente para garantir a segurança e a estabilidade durante todo o processo de remoção das peças danificadas e instalação dos novos perfis.

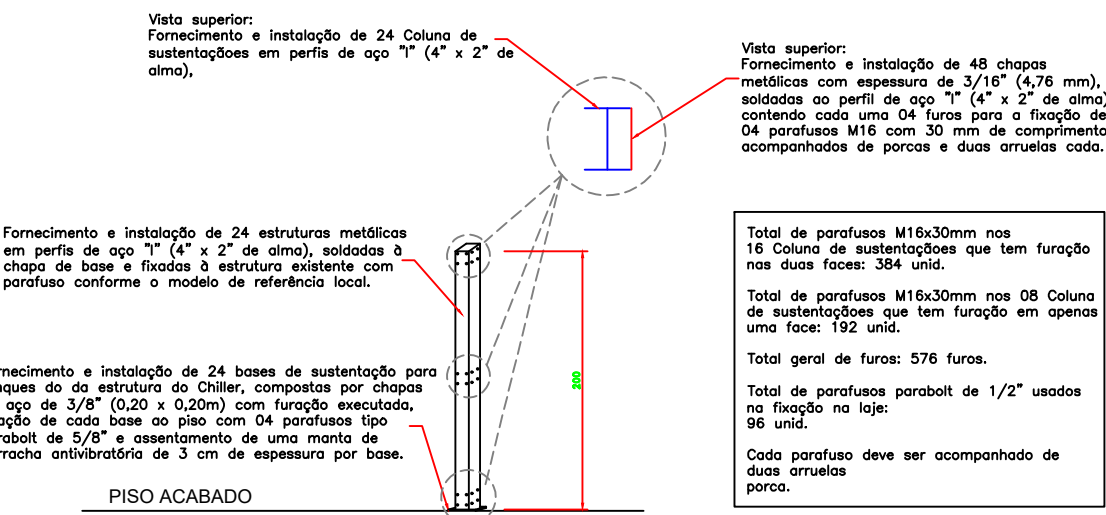


DETALHE 01 - NOVO SUPORTE DE SUSTENTAÇÃO DO MÓDULO DO CHILLER

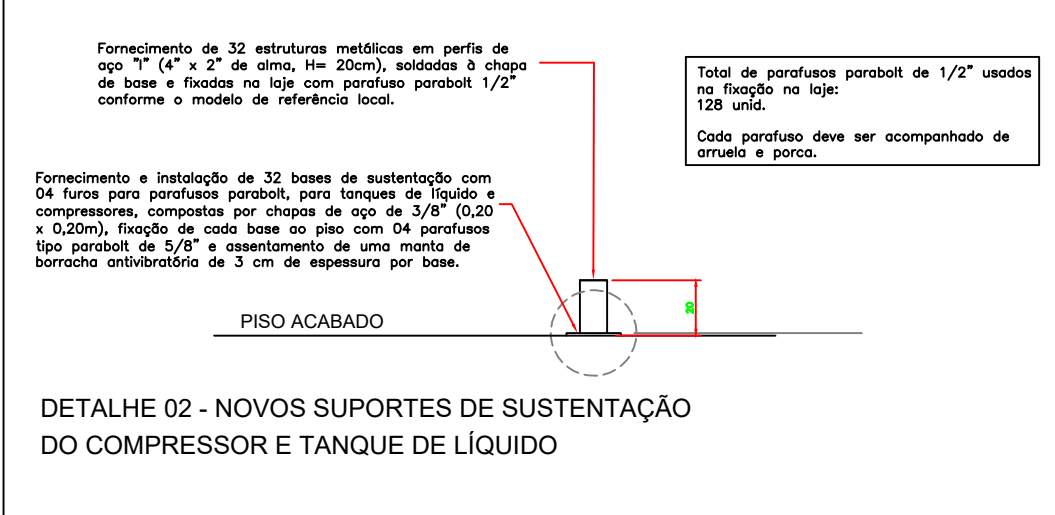


DETALHE 02 - NOVOS SUPORTES DE SUSTENTAÇÃO DO COMPRESSOR E TANQUE DE LÍQUIDO

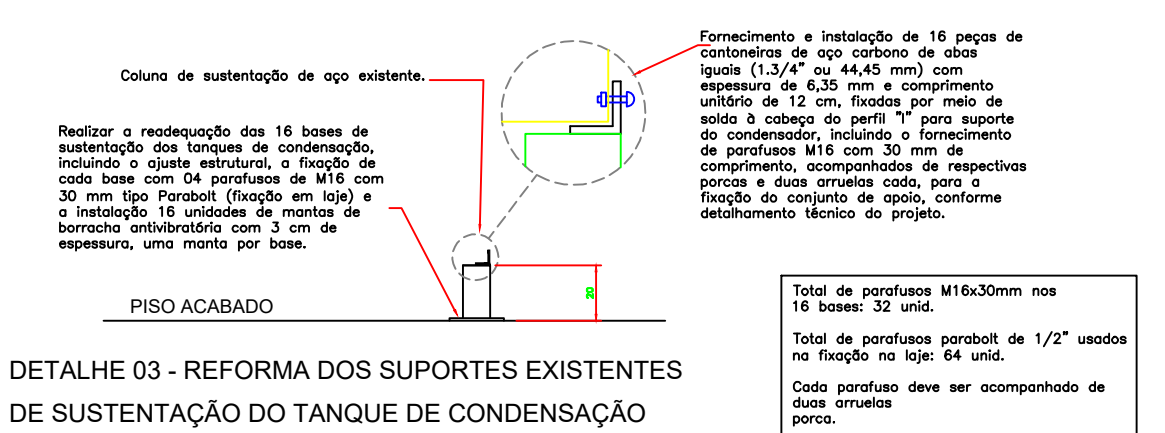


DETALHE 03 - REFORMA DOS SUPORTES EXISTENTES DE SUSTENTAÇÃO DO TANQUE DE CONDENSAÇÃO

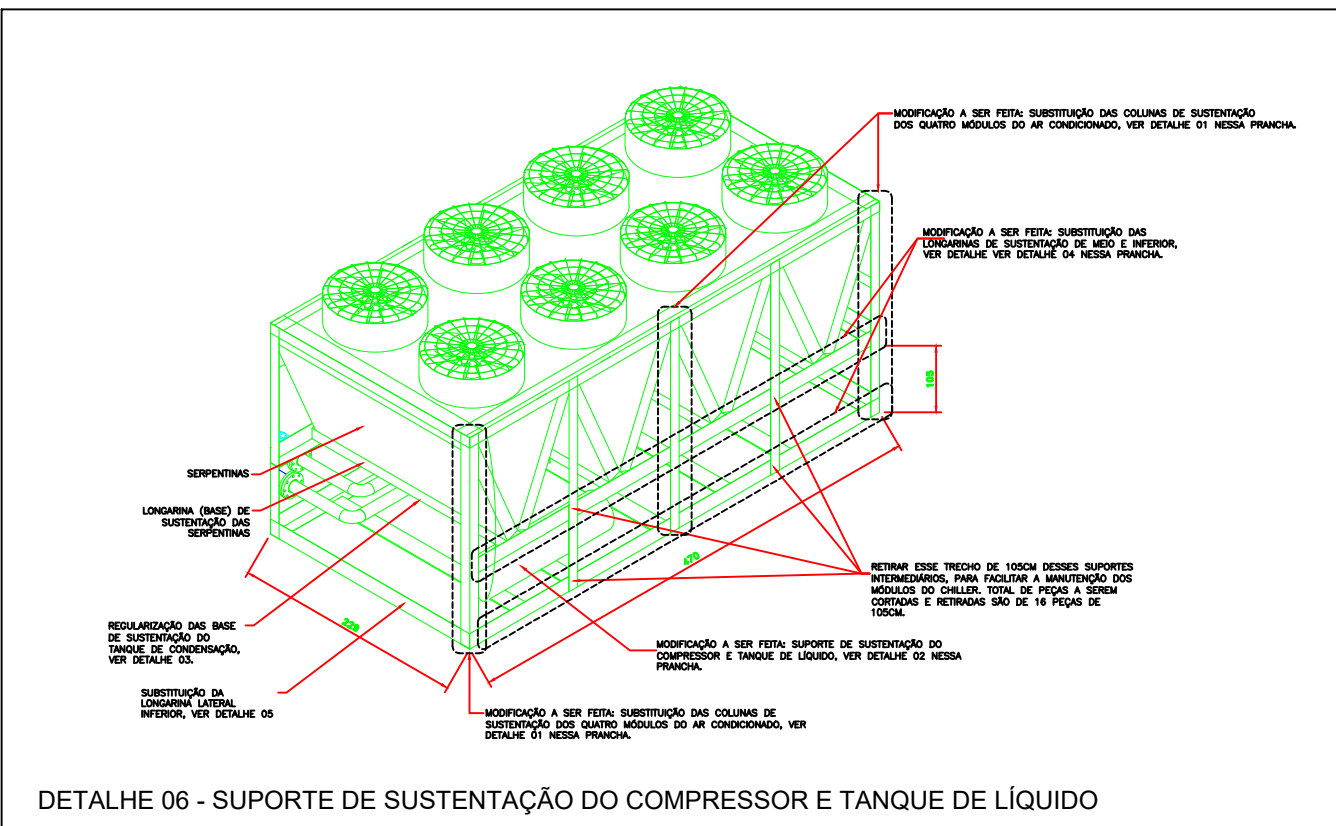

DETALHE 06 - SUPORTE DE SUSTENTAÇÃO DO COMPRESSOR E TANQUE DE LÍQUIDO

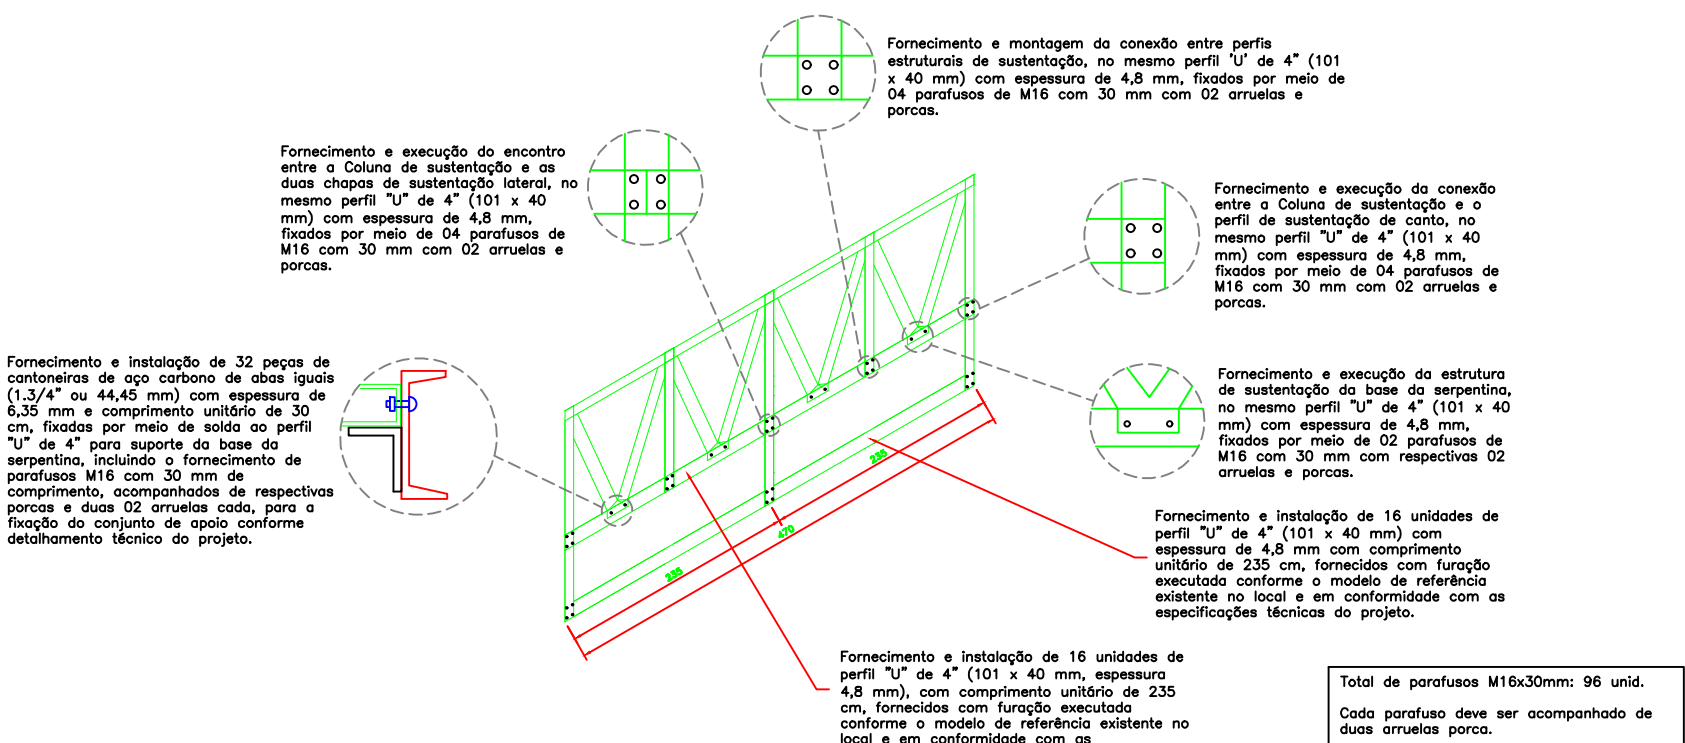

DETALHE 04 - SUBSTITUIÇÃO DA LONGARINA DE SUSTENTAÇÃO DAS SERPENTINAS E TRAVAMENTO FRONTAL MEIO E INFERIOR

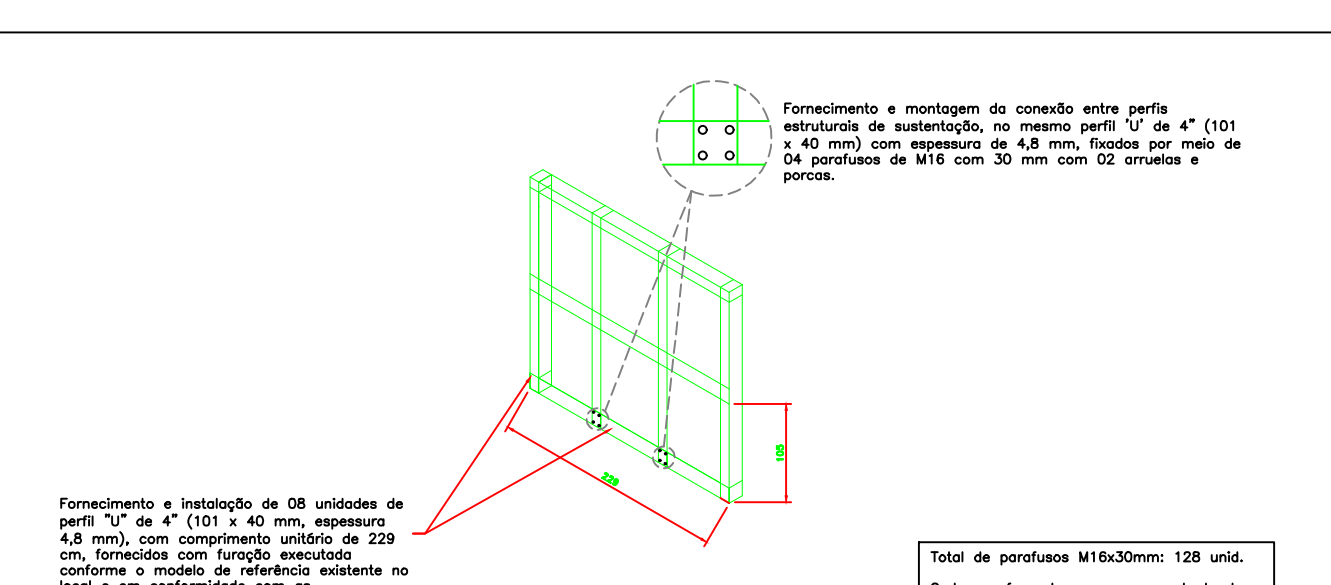

DETALHE 05 - SUBSTITUIÇÃO DA LONGARINA TRAVAMENTO LATERAL INFERIOR

*OBSERVAÇÃO IMPORTANTE: TODAS AS MEDIDAS E COTAS DEVERÃO SER CONFERIDAS PELO EXECUTOR, NO LOCAL DO SERVIÇO, CASO SEJA NECESSÁRIO ALGUM AJUSTE. O EXECUTOR DEVERÁ INFORMAR À FISCALIZAÇÃO PARA SUA APROVAÇÃO.

REVISÃO	MODIFICAÇÃO	DATA	PROJETA	DESENHISTA	APROV
1					
2					
