




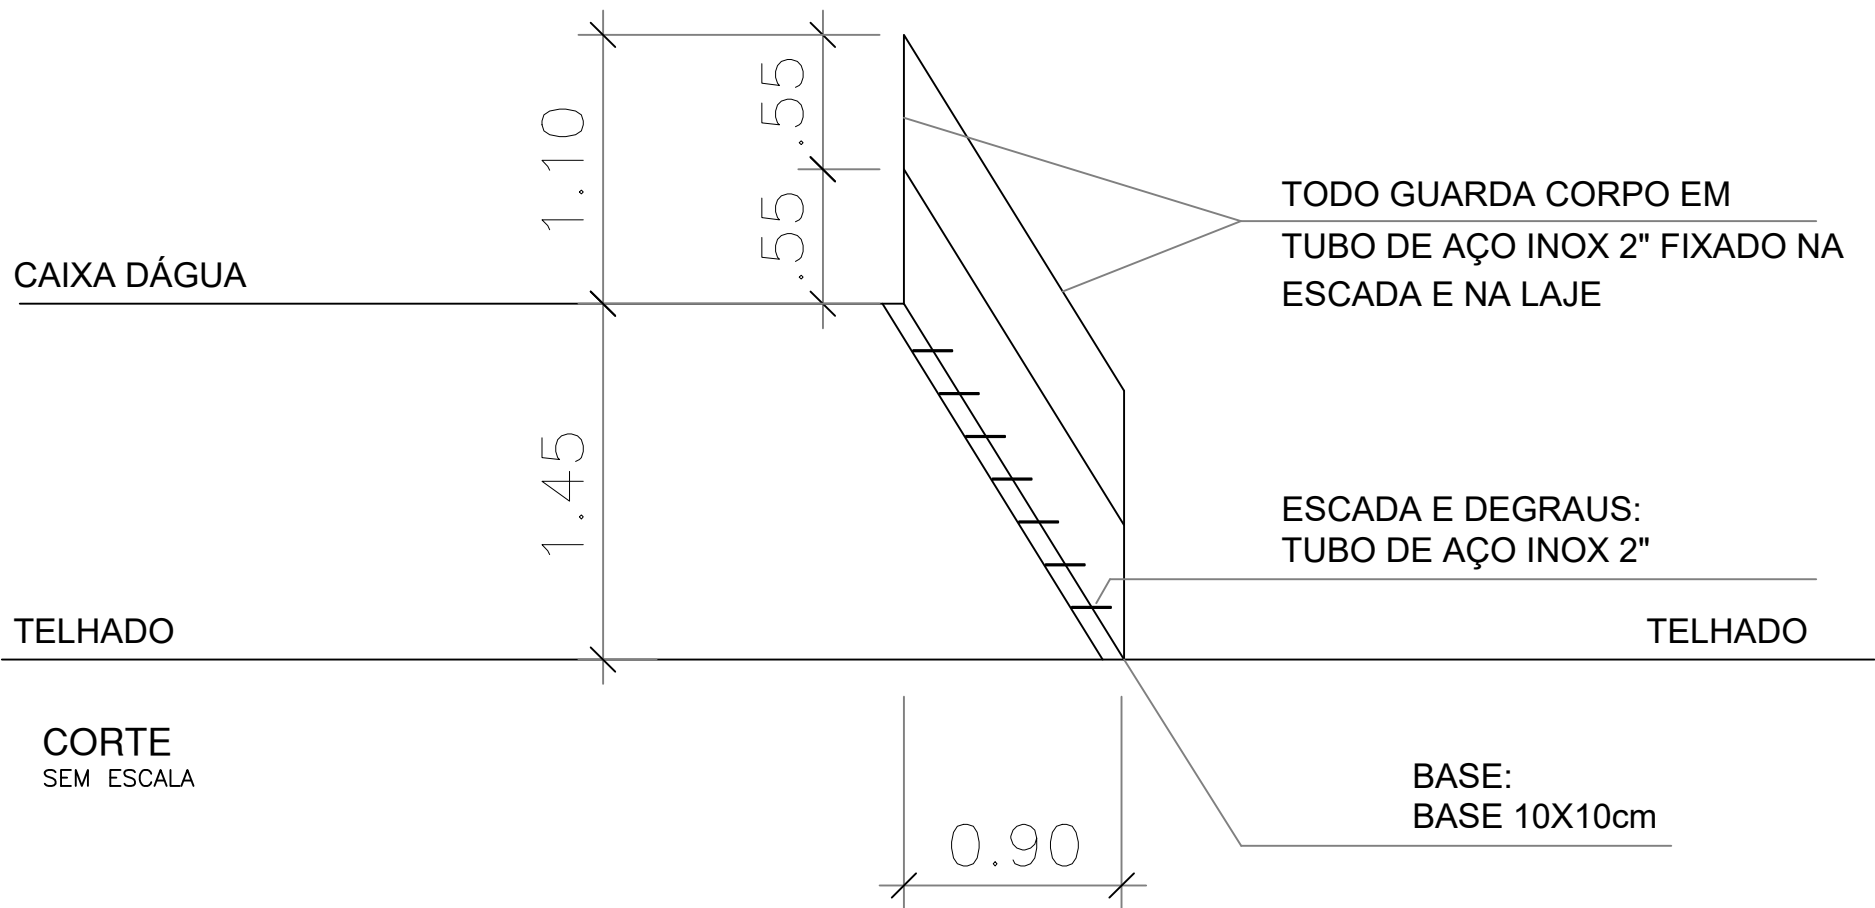


DETALHE - ESCADA DE INSTALAÇÃO DE ESCADA NO TELHADO

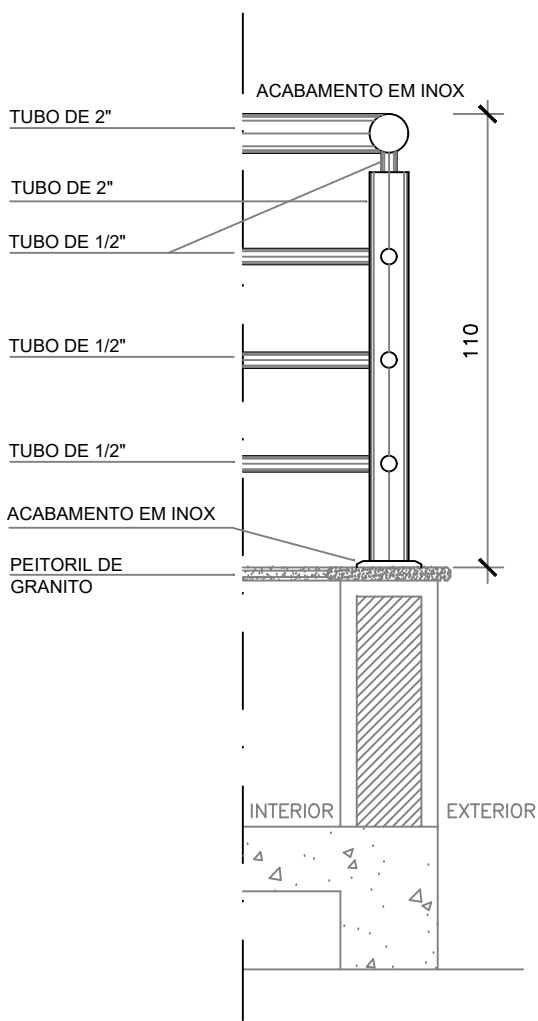

CORTE
SEM ESCALA

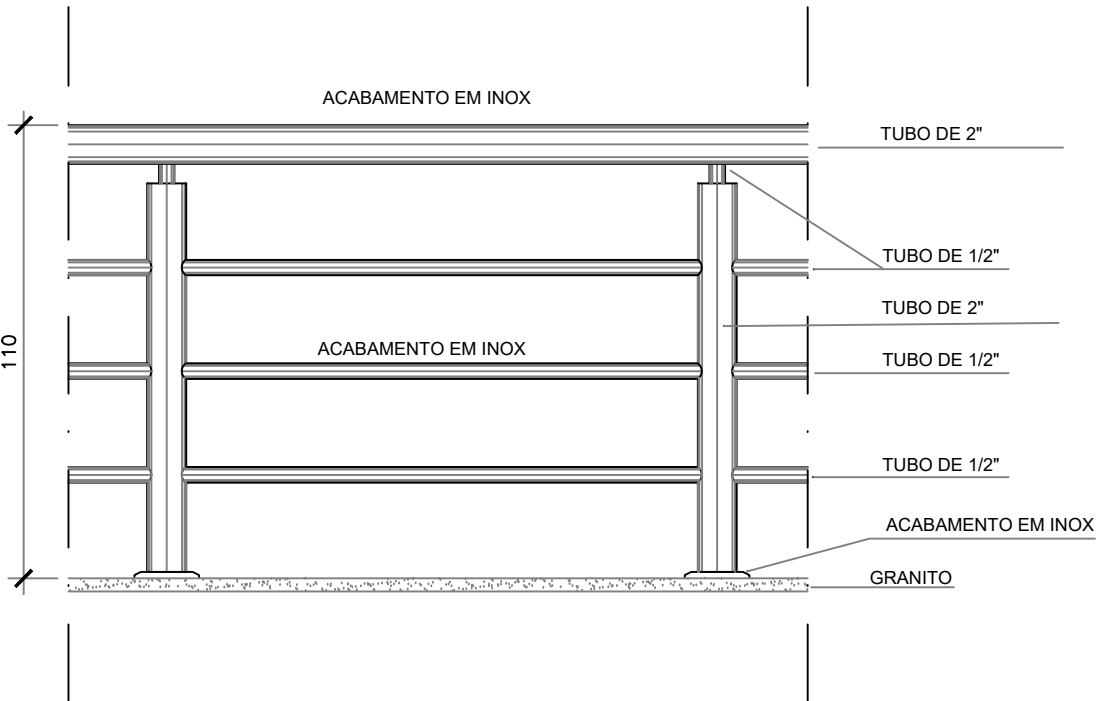

VISTA FRONTAL
SEM ESCALA

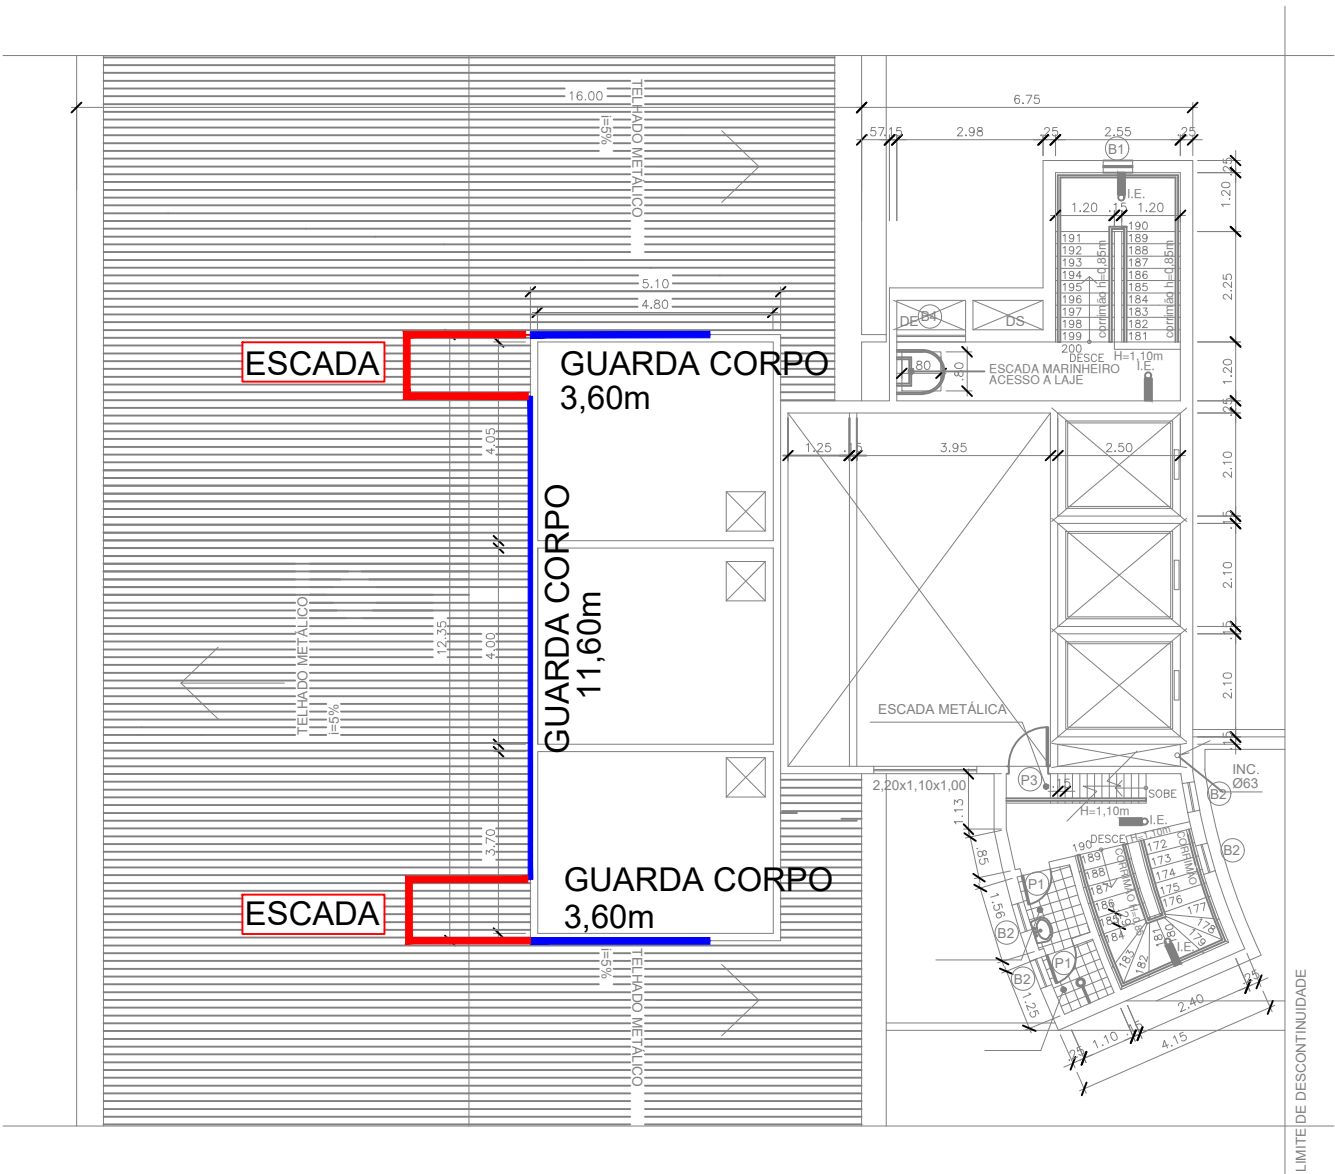

PLANTA BAIXA - POSICIONAMENTO NA COBERTURA
SEM ESCALA

DETALHE - INSTALAÇÃO DE GUARDA-CORPO NA COBERTURA

EMISSÃO INICIAL	-
REV.	MODIFICAÇÃO